


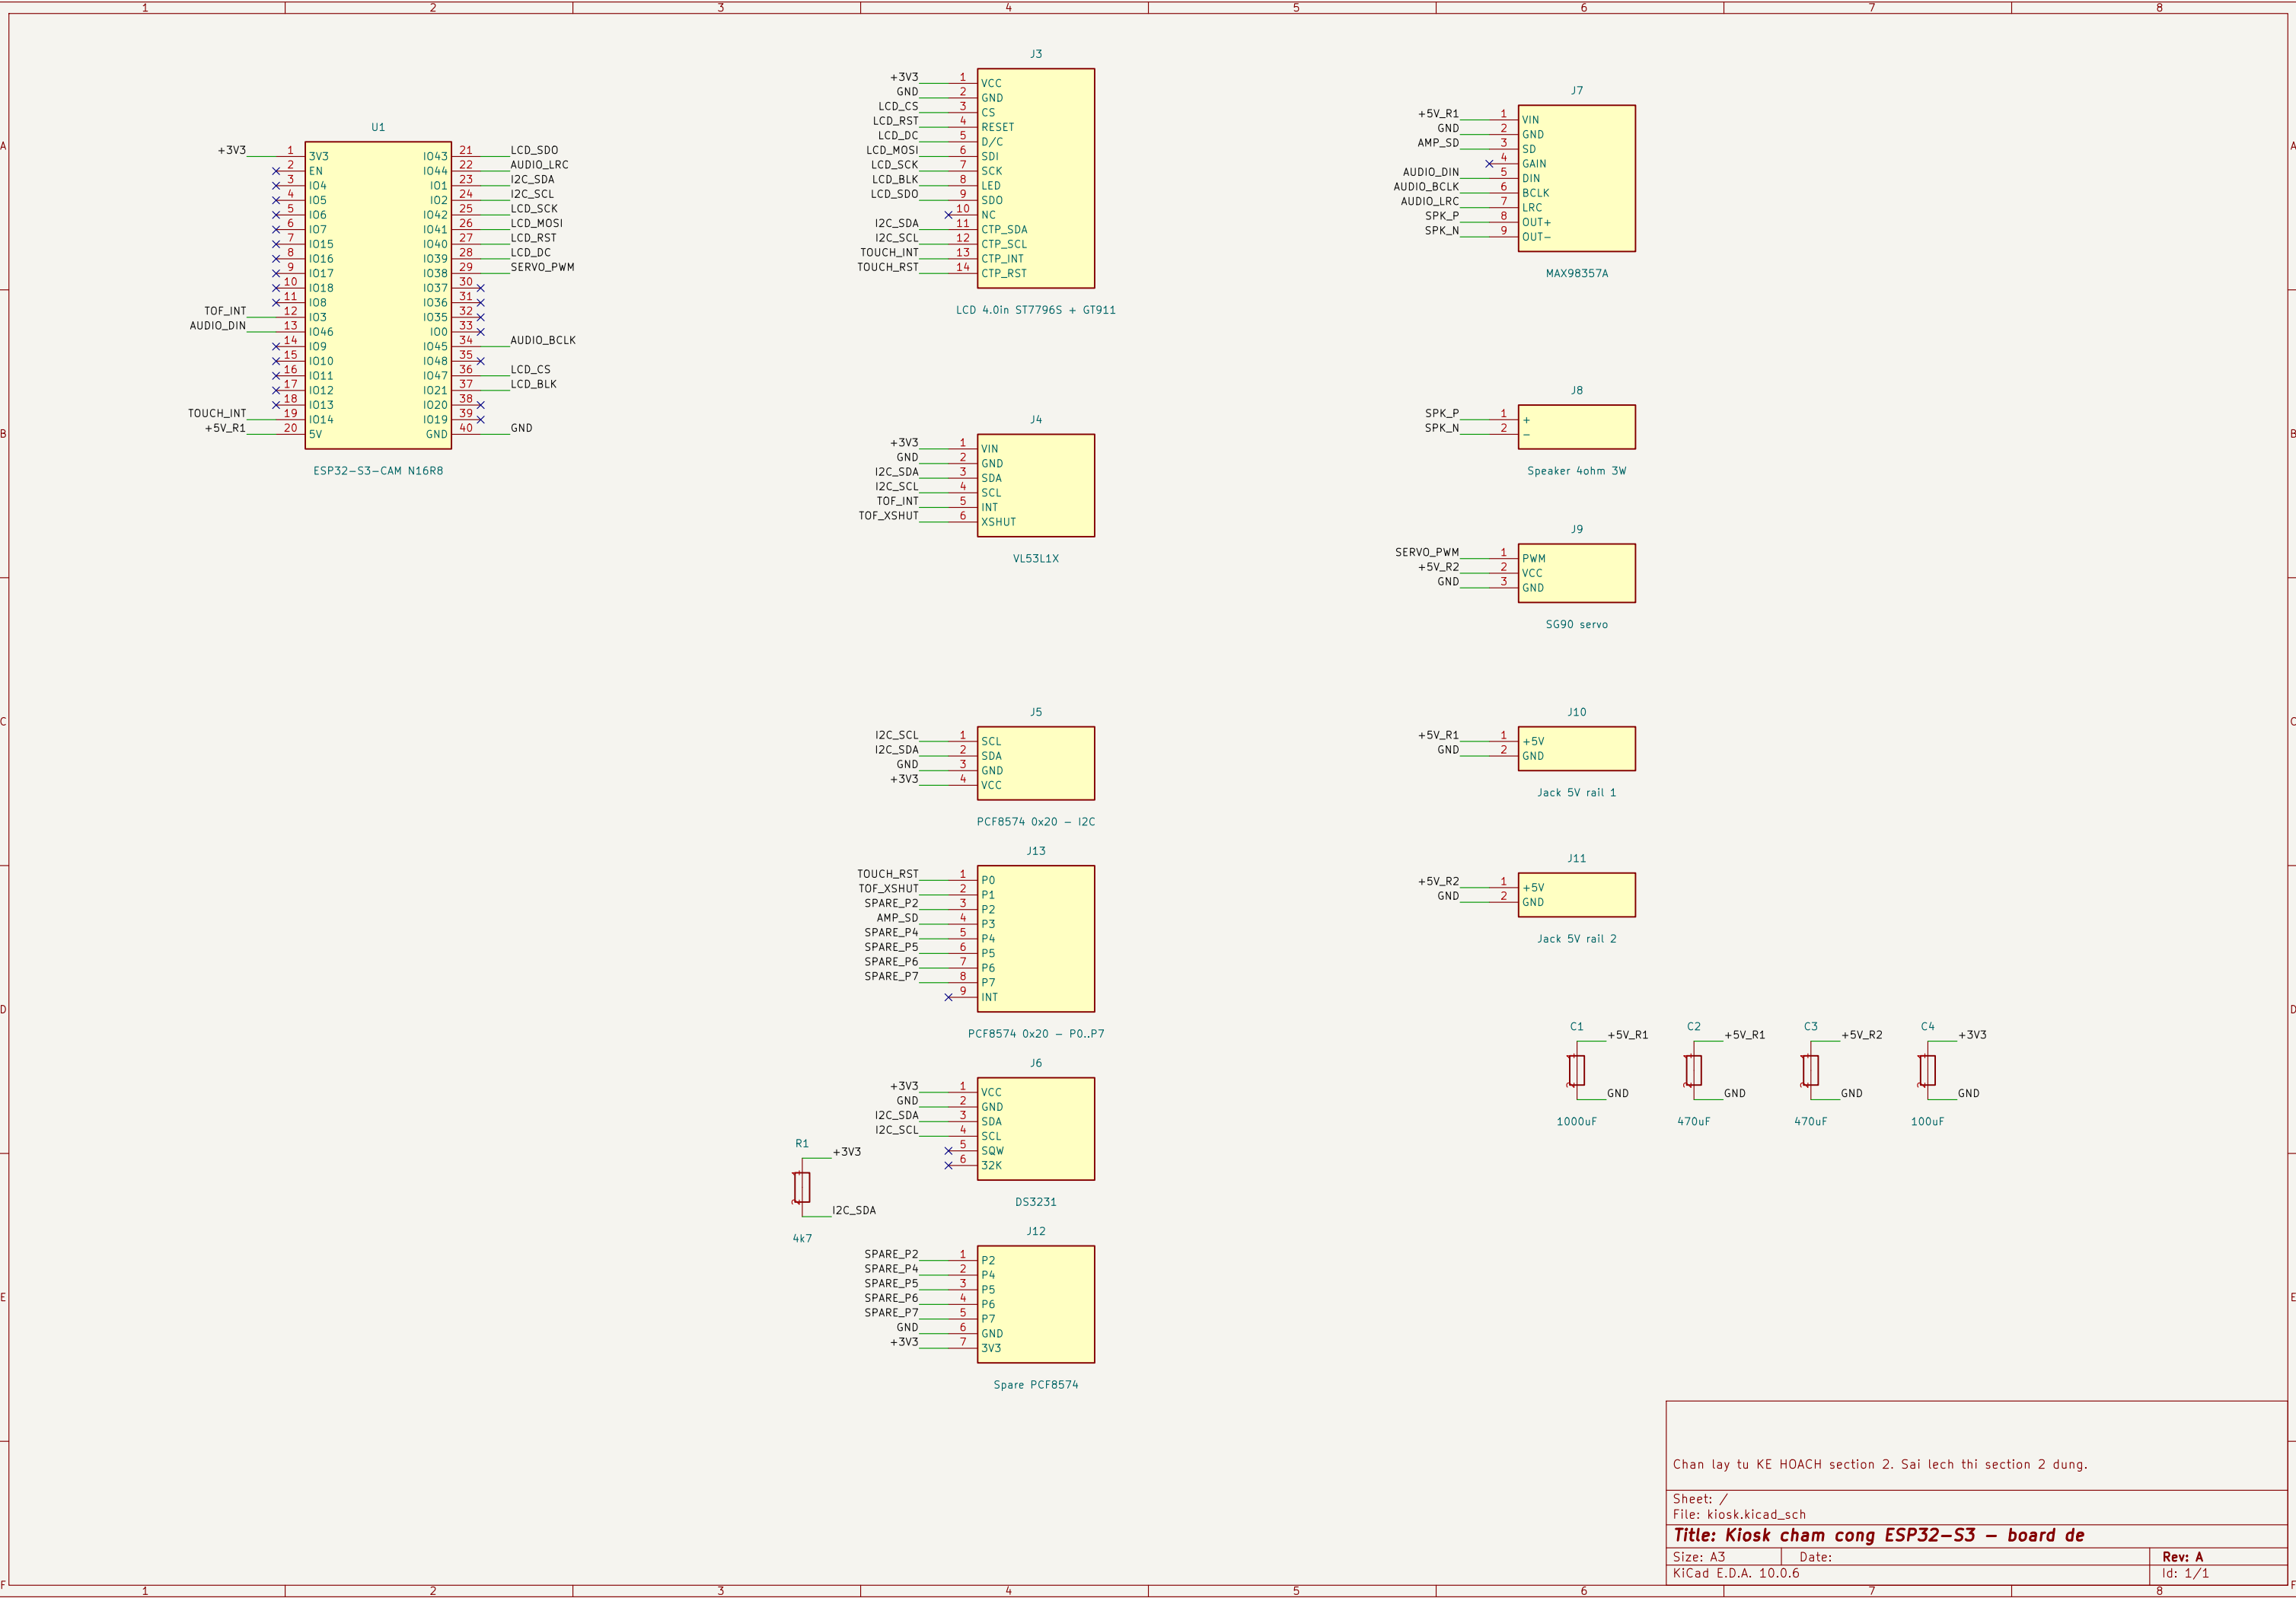

Chan lay tu KE HOACH section 2. Sai lech thi section 2 dung.